



REV	DESCRIPTION	DATE	BY
P1	Making sketch	2026-10-03	AC
P2	Surplus pipe checks before buying (decision 42B)	2026-10-03	AC

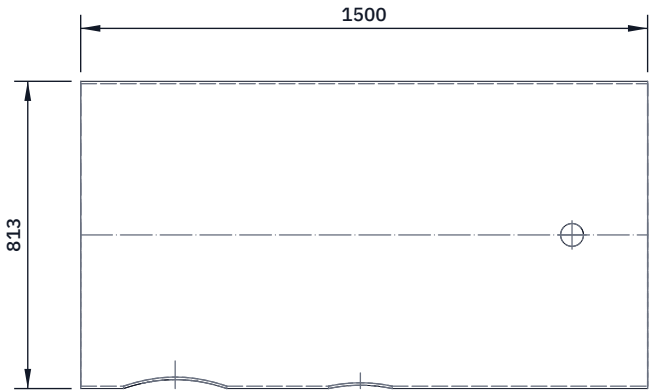


TOP VIEW

Scale 1:20; looking down (along -Z)

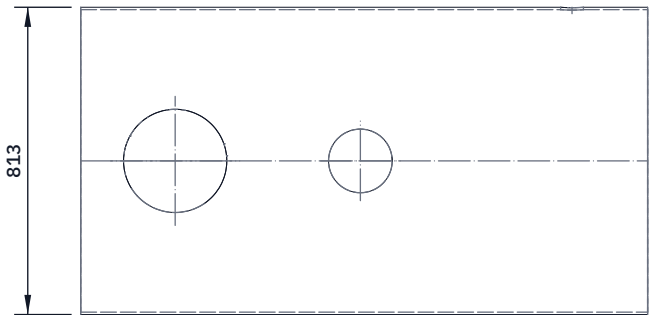


FRONT VIEW

Scale 1:20; looking at the front (along +Y)

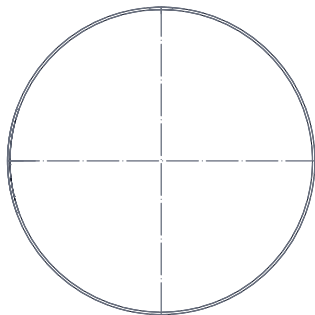

RIGHT VIEW

Scale 1:20; looking at the right side (along -X)

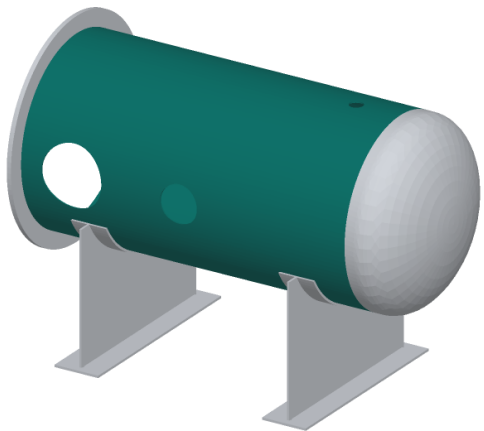

WHERE IT GOES

This part in colour, its neighbours in grey

HOW TO MAKE IT AND HOW IT FITS

Surplus offcut: before buying, check it is round within 8 mm (largest less smallest diameter) and the wall is 5.9 or more at 8 points round each end; reject a dented or pitted pipe
Cut the pipe 1,500 long, ends square within 1 mm
Mark a line along the top; hole centres measured from the door end:
window hole 273.1 dia at 250, on the side 90 deg from the top
feed-through hole 168.3 dia at 740, same side as the window
manifold hole 60.3 dia at 1300, on the top line
Cut each hole to the nozzle's outside size plus 1 to 2 mm, square to the axis; grind smooth; bevel the outside edge for the fillet weld
Saddles, rails, tabs, ring and head are welded on (assembly steps 1 to 5)
Check: holes on the right side and line; nozzle stubs slide in

ALTIRIG

github.com/BoujeeEnjinia1701/altirig

AltiRig shell: pipe offcut with nozzle holes

DRAWING NO. ALR-DWG-101			REV P2	SHEET 1 of 1	SIZE ANSI B
SCALE 1:20	UNITS mm	PROJECTION 	DATE 2026-10-03	DRAWN Amish Chadha	

MATERIAL / NOTES Steel pipe 813 OD x 6.35 wall (32 in x 1/4 in), 1,500 long					
---	--	--	--	--	--